


C:\Users\koster\Documents\Online_FSB-NELV_Central_R18_allenfordster.txt	
---	--

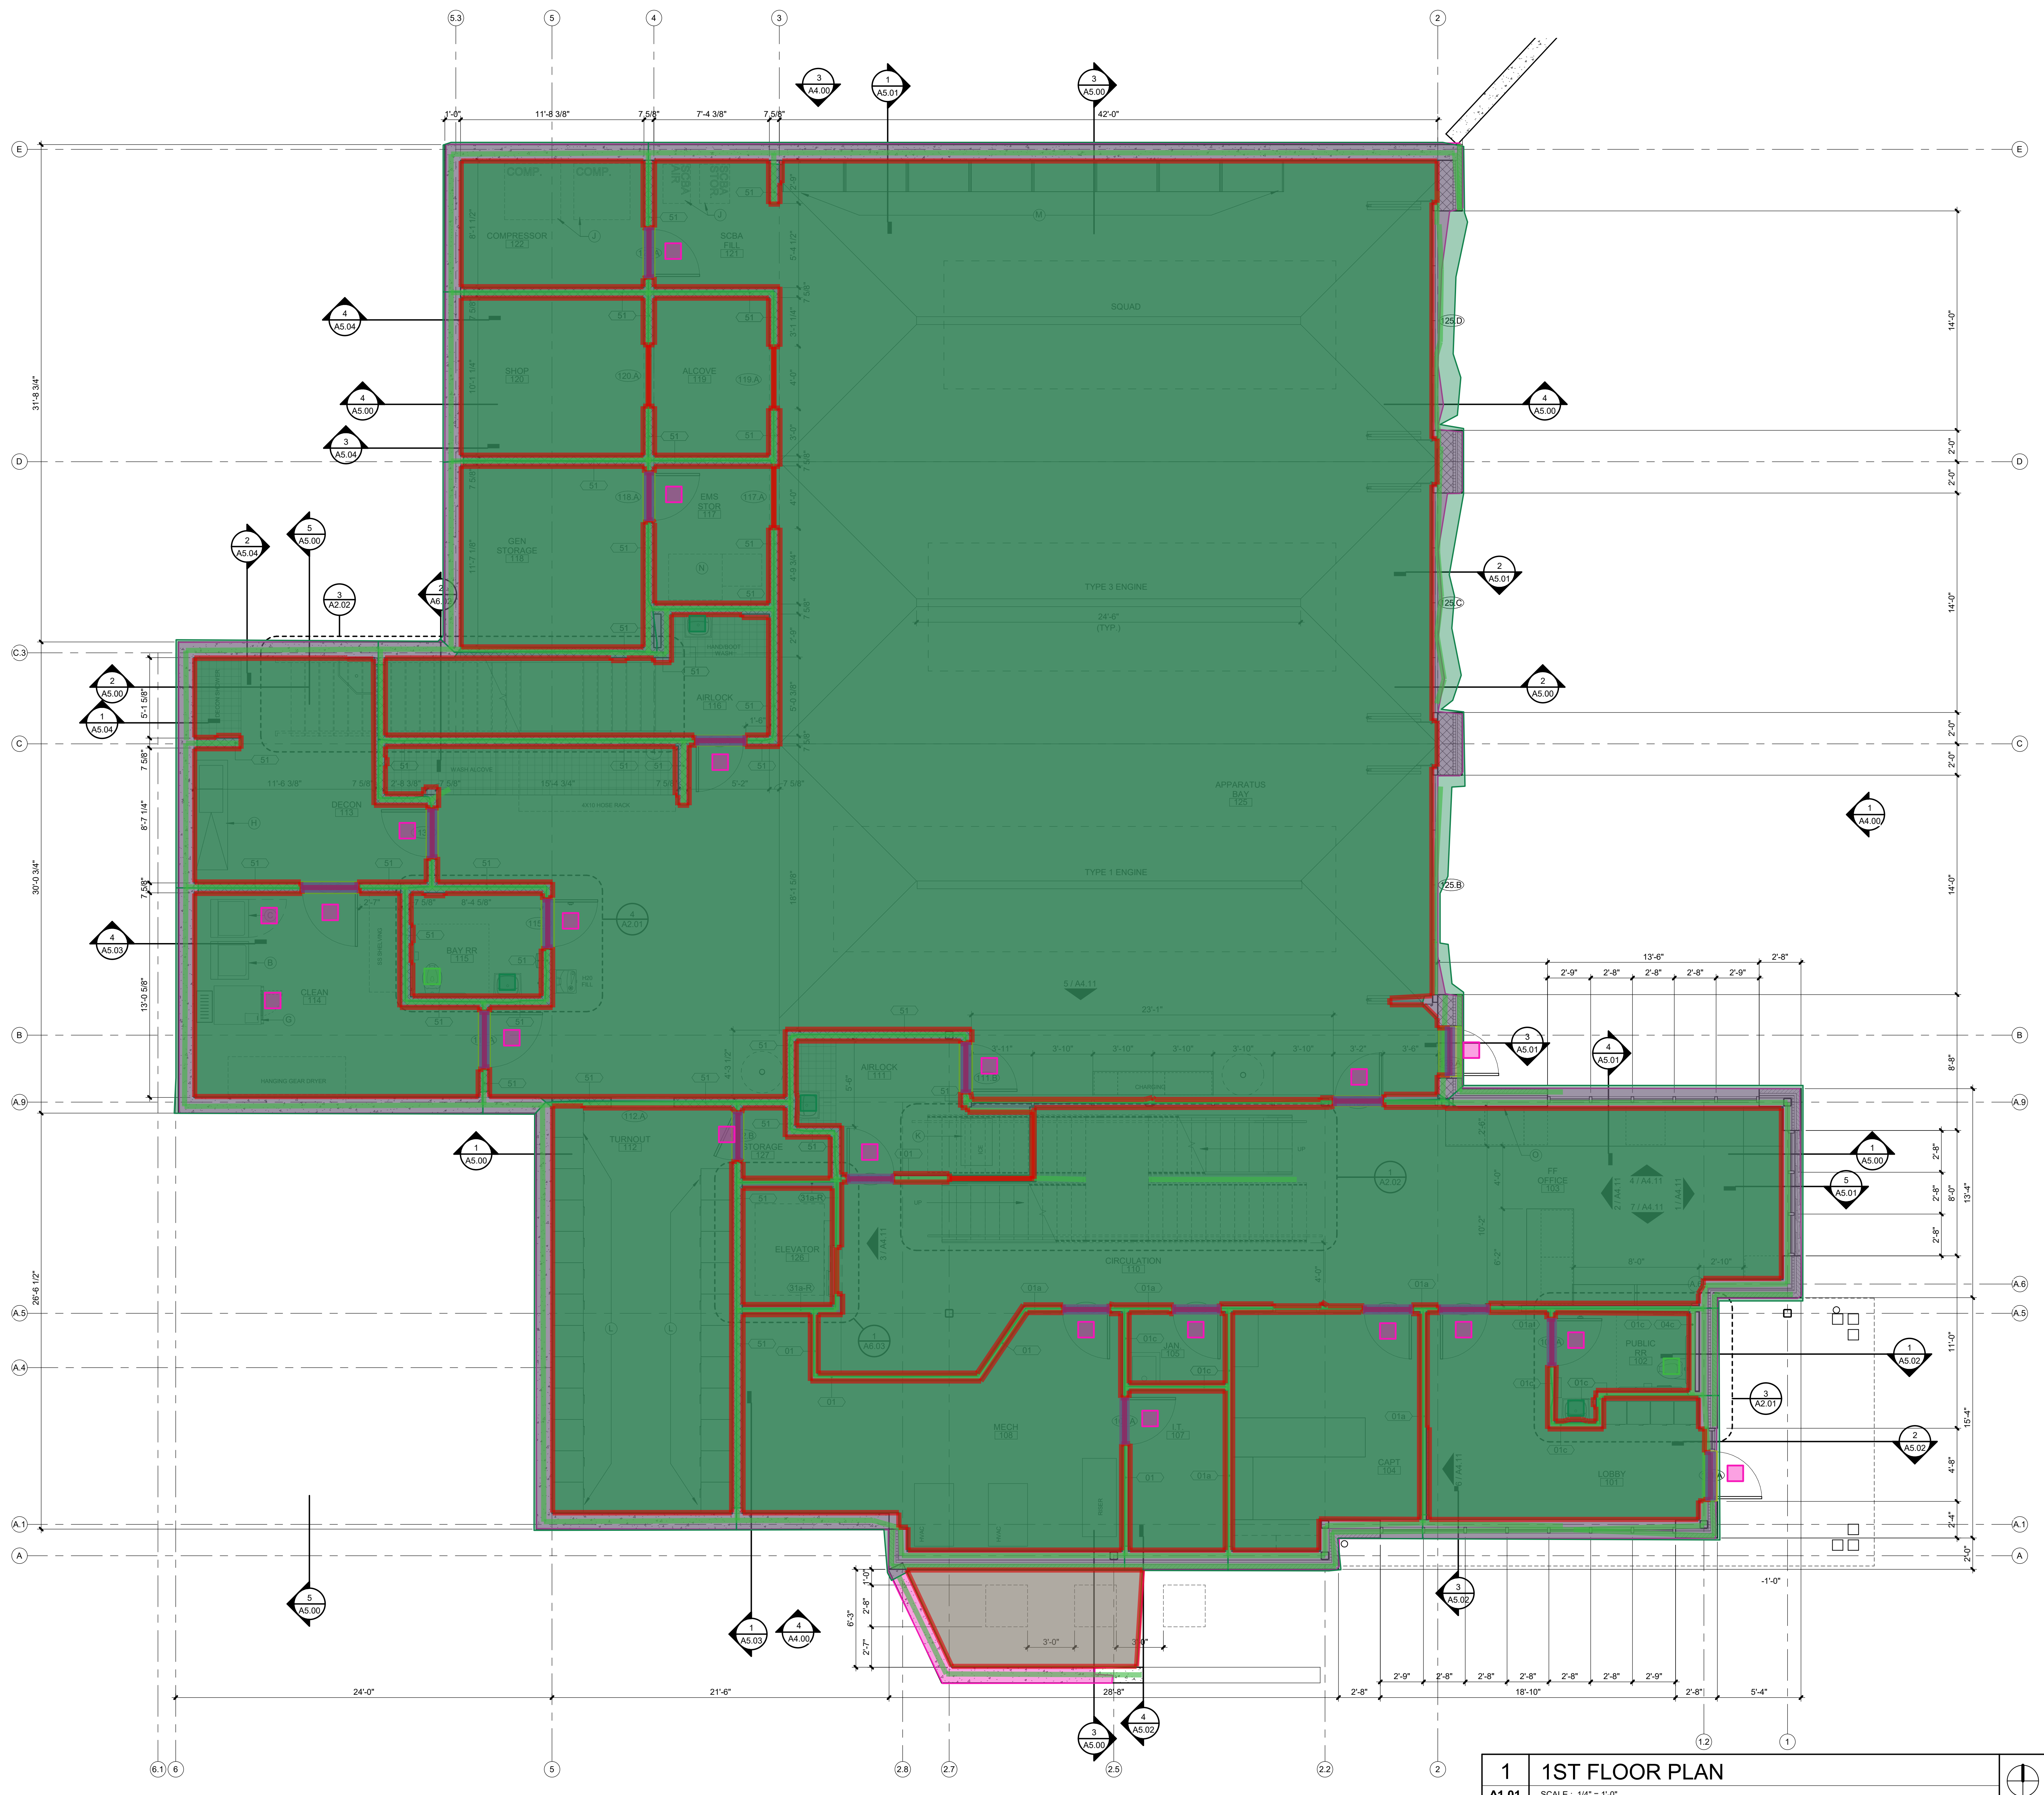

Olathe Fire
Station No. 8
14700 Lakeshore Dr
Olathe KS



No.:	19003
	02.17.2020
For:	DESIGN DEVELOPMENT

[illegible]

REGISTRATION

FOR CONSTRUCTION

PROJECT TEAM

PROJECT	FINKLE+WILLIAMS ARCHITECTURE
CONSULTANT	TCA ARCHITECTS
OWNER	SK DESIGN GROUP
SCOPE	SWT DESIGN
CULTURAL	BOB D. CAMPBELL
TRAINING	LANKFORD FINKLE
MECHANICAL	LANKFORD FINKLE
ELECTRICAL	LANKFORD FINKLE
CONTRACTOR	TURNER CONSTRUCTION

KLE + WILLIAM
ARCHITECTS

College Blvd, Suite
land Park, Kansas 66
98-1550


SHEET TITLE

FIRST FLOOR PLAN

SHEET NUMBER

A1.01

Total areas		
 Footprint 1		7,208 SF
 Net area 30		6,547 SF
 Doors area 25		51 SF
 Gross area 29		7,262 SF
 Gross Internal Area ...		296,803 SF
Total lines		
 Doors centerline 25		76 FT
 Wall centerline 154		1,032 FT
 Wall Perimeter 30		1,466 FT
Total counts		
 Toilet 5		5 EA
 Sink 5		5 EA
 Single Swing Door 25		25 EA
 Double Swing Door 11		11 EA
 Urinals 1		1 EA
 Cooktop 1		1 EA

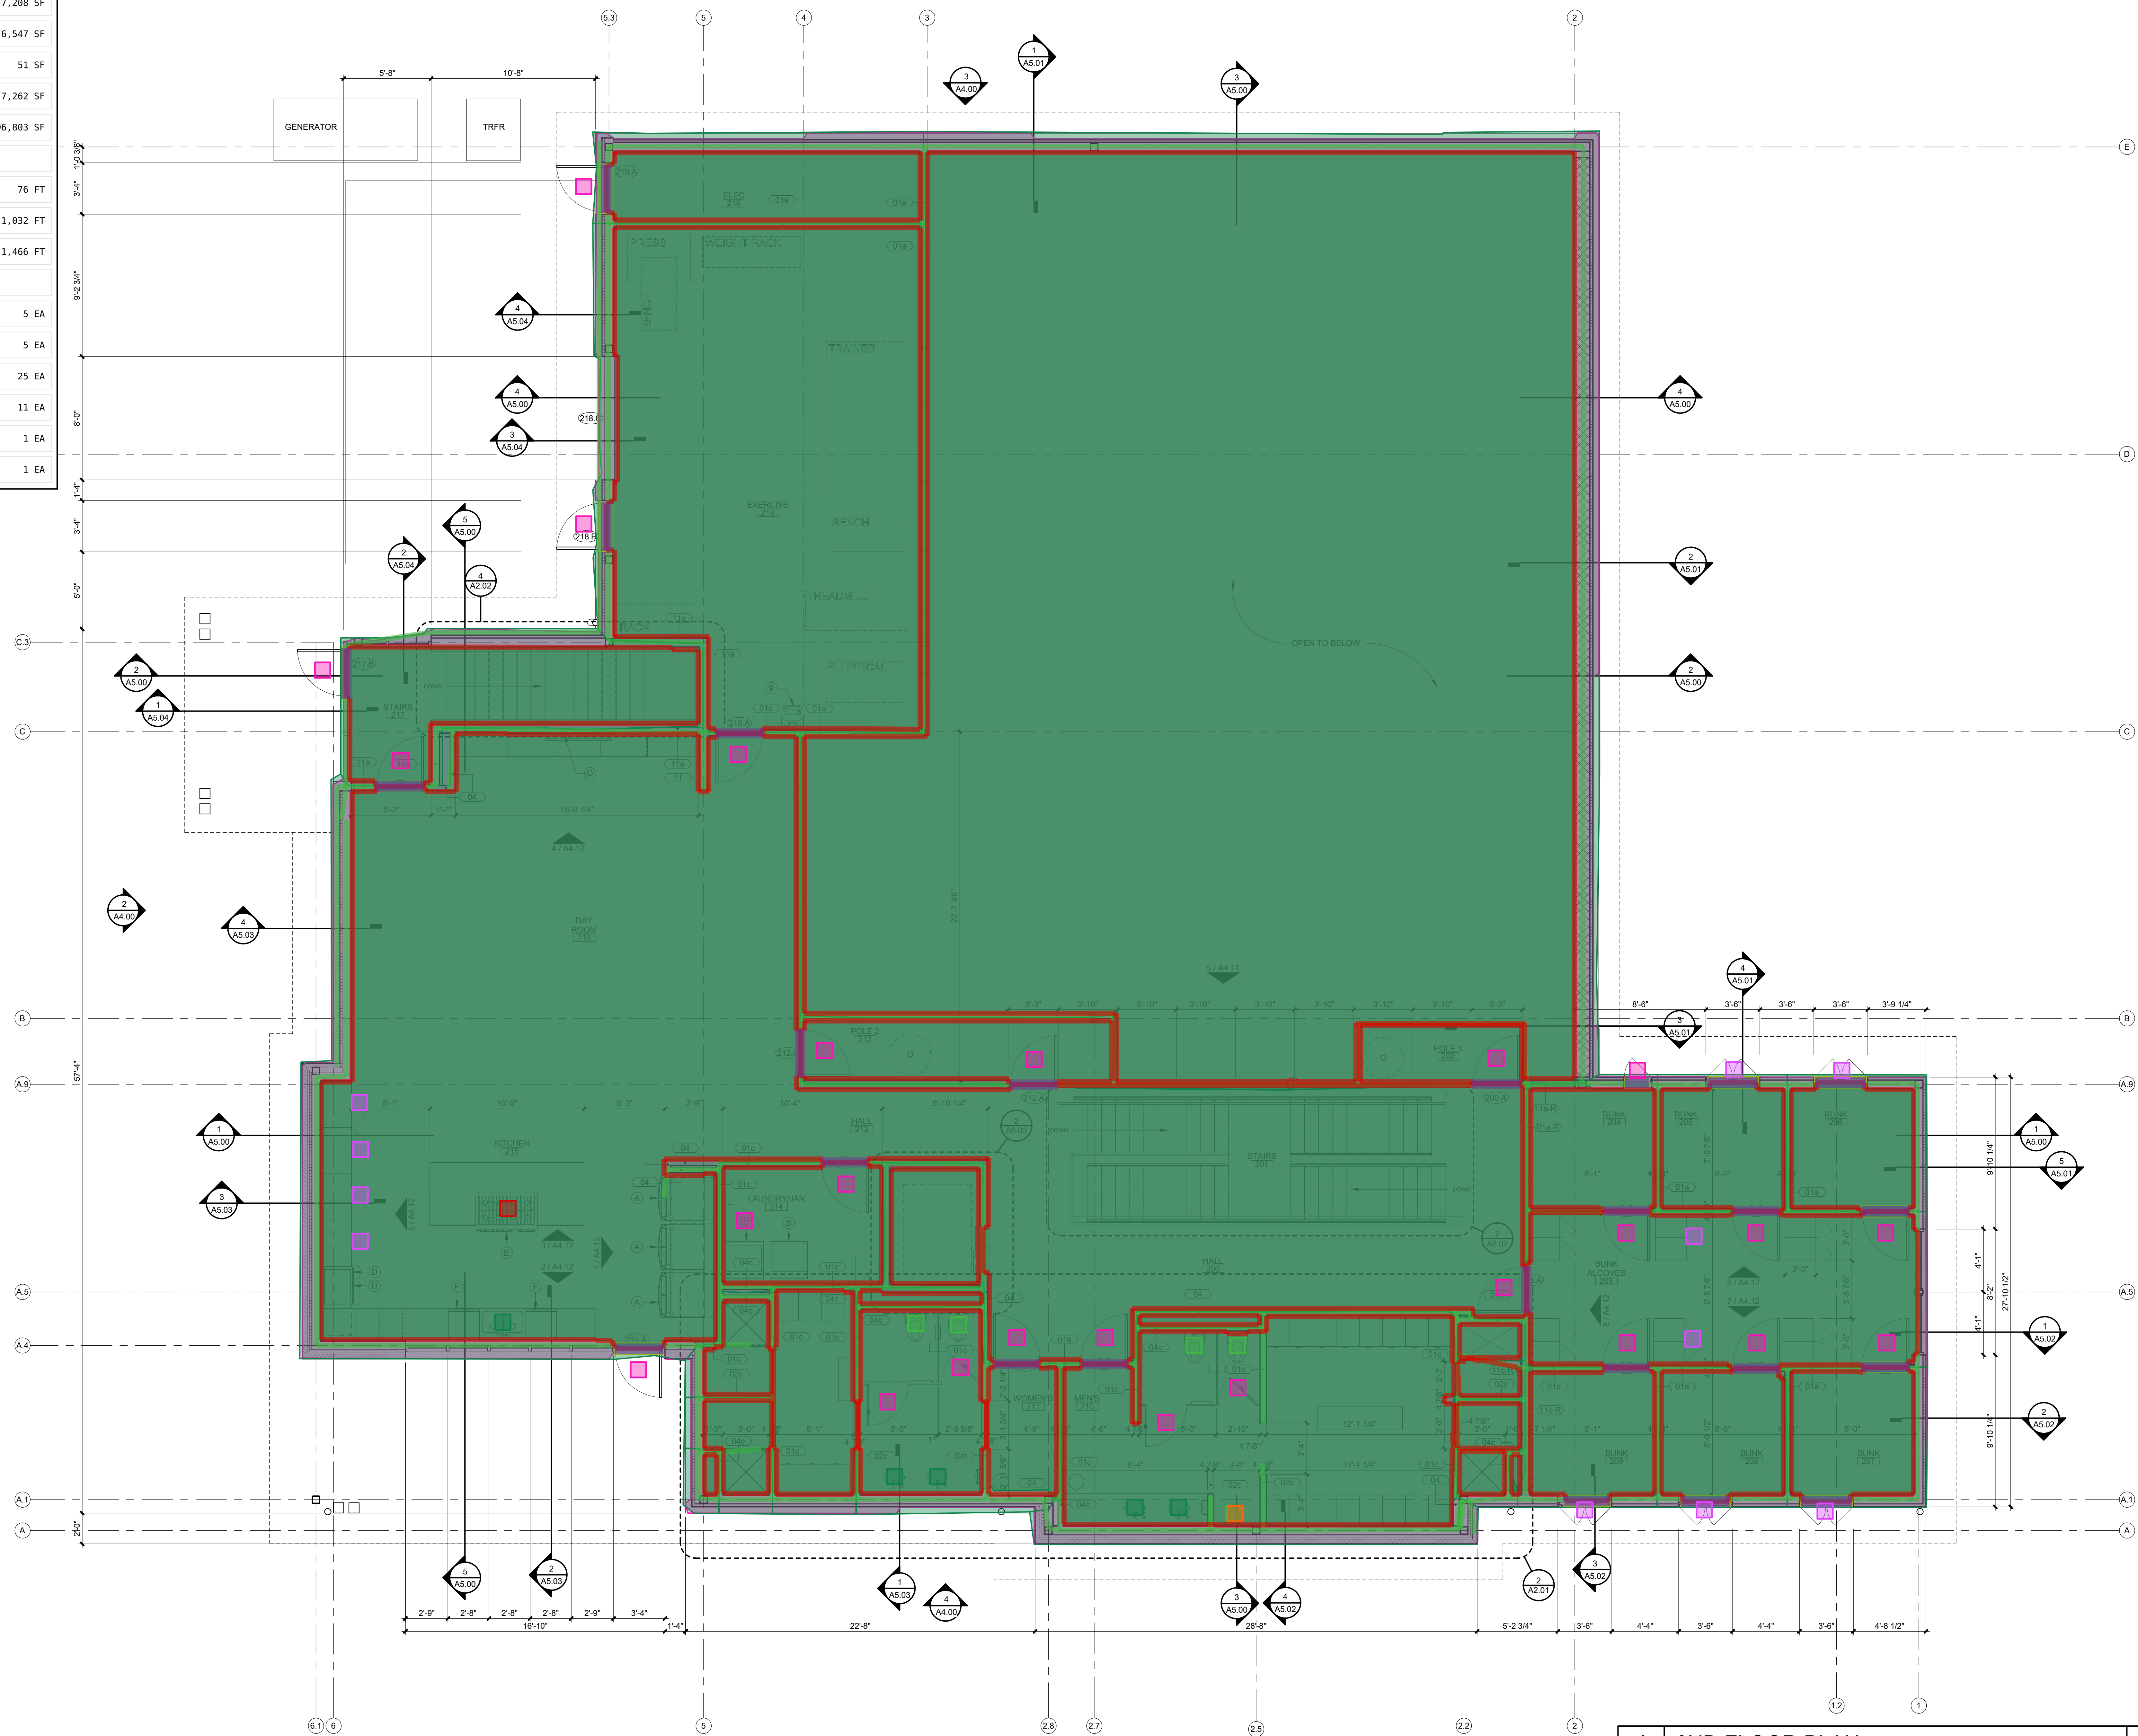

Olathe Fire
Station No. 8
14700 Lakeshore Dr
Olathe KS



Project No.:	19003
Date:	02.17.2020
Issued For:	DESIGN DEVELOPMENT

[illegible]

REGISTRATION

NOT FOR CONSTRUCTION

PROJECT TEAM	
ARCHITECT	FINKLE+WILLIAMS ARCHITECTURE
ENGINEERING CONSULTANT	TCA ARCHITECTS
CIVIL	SK DESIGN GROUP
LANDSCAPE	SWT DESIGN
STRUCTURAL	BOB D. CAMPBELL
PLUMBING	LANKFORD FRIEDMAN
MECHANICAL	LANKFORD FRIEDMAN
ELECTRICAL	LANKFORD FRIEDMAN
CONTRACTOR	TURNER CONSTRUCTION

FINKLE + WILLIAM
ARCHITECTS

1007 College Blvd, Suite 100
Overland Park, Kansas 66204
913+498-1550

SHEET TITLE

SECOND FLOOR PLAN

SHEET NUMBER

A1.02