


Total areas		
Footprint	1	733 SF
Net area	13	617 SF
Doors area	1	1 SF
Gross area	12	664 SF
Gross Internal Area (GIA)		12591 SF
Total lines		
Doors centerline	1	2 FT
Wall centerline	59	382 FT
Wall Perimeter	14	385 FT
Total counts		
Single Swing Door	14	14 EA

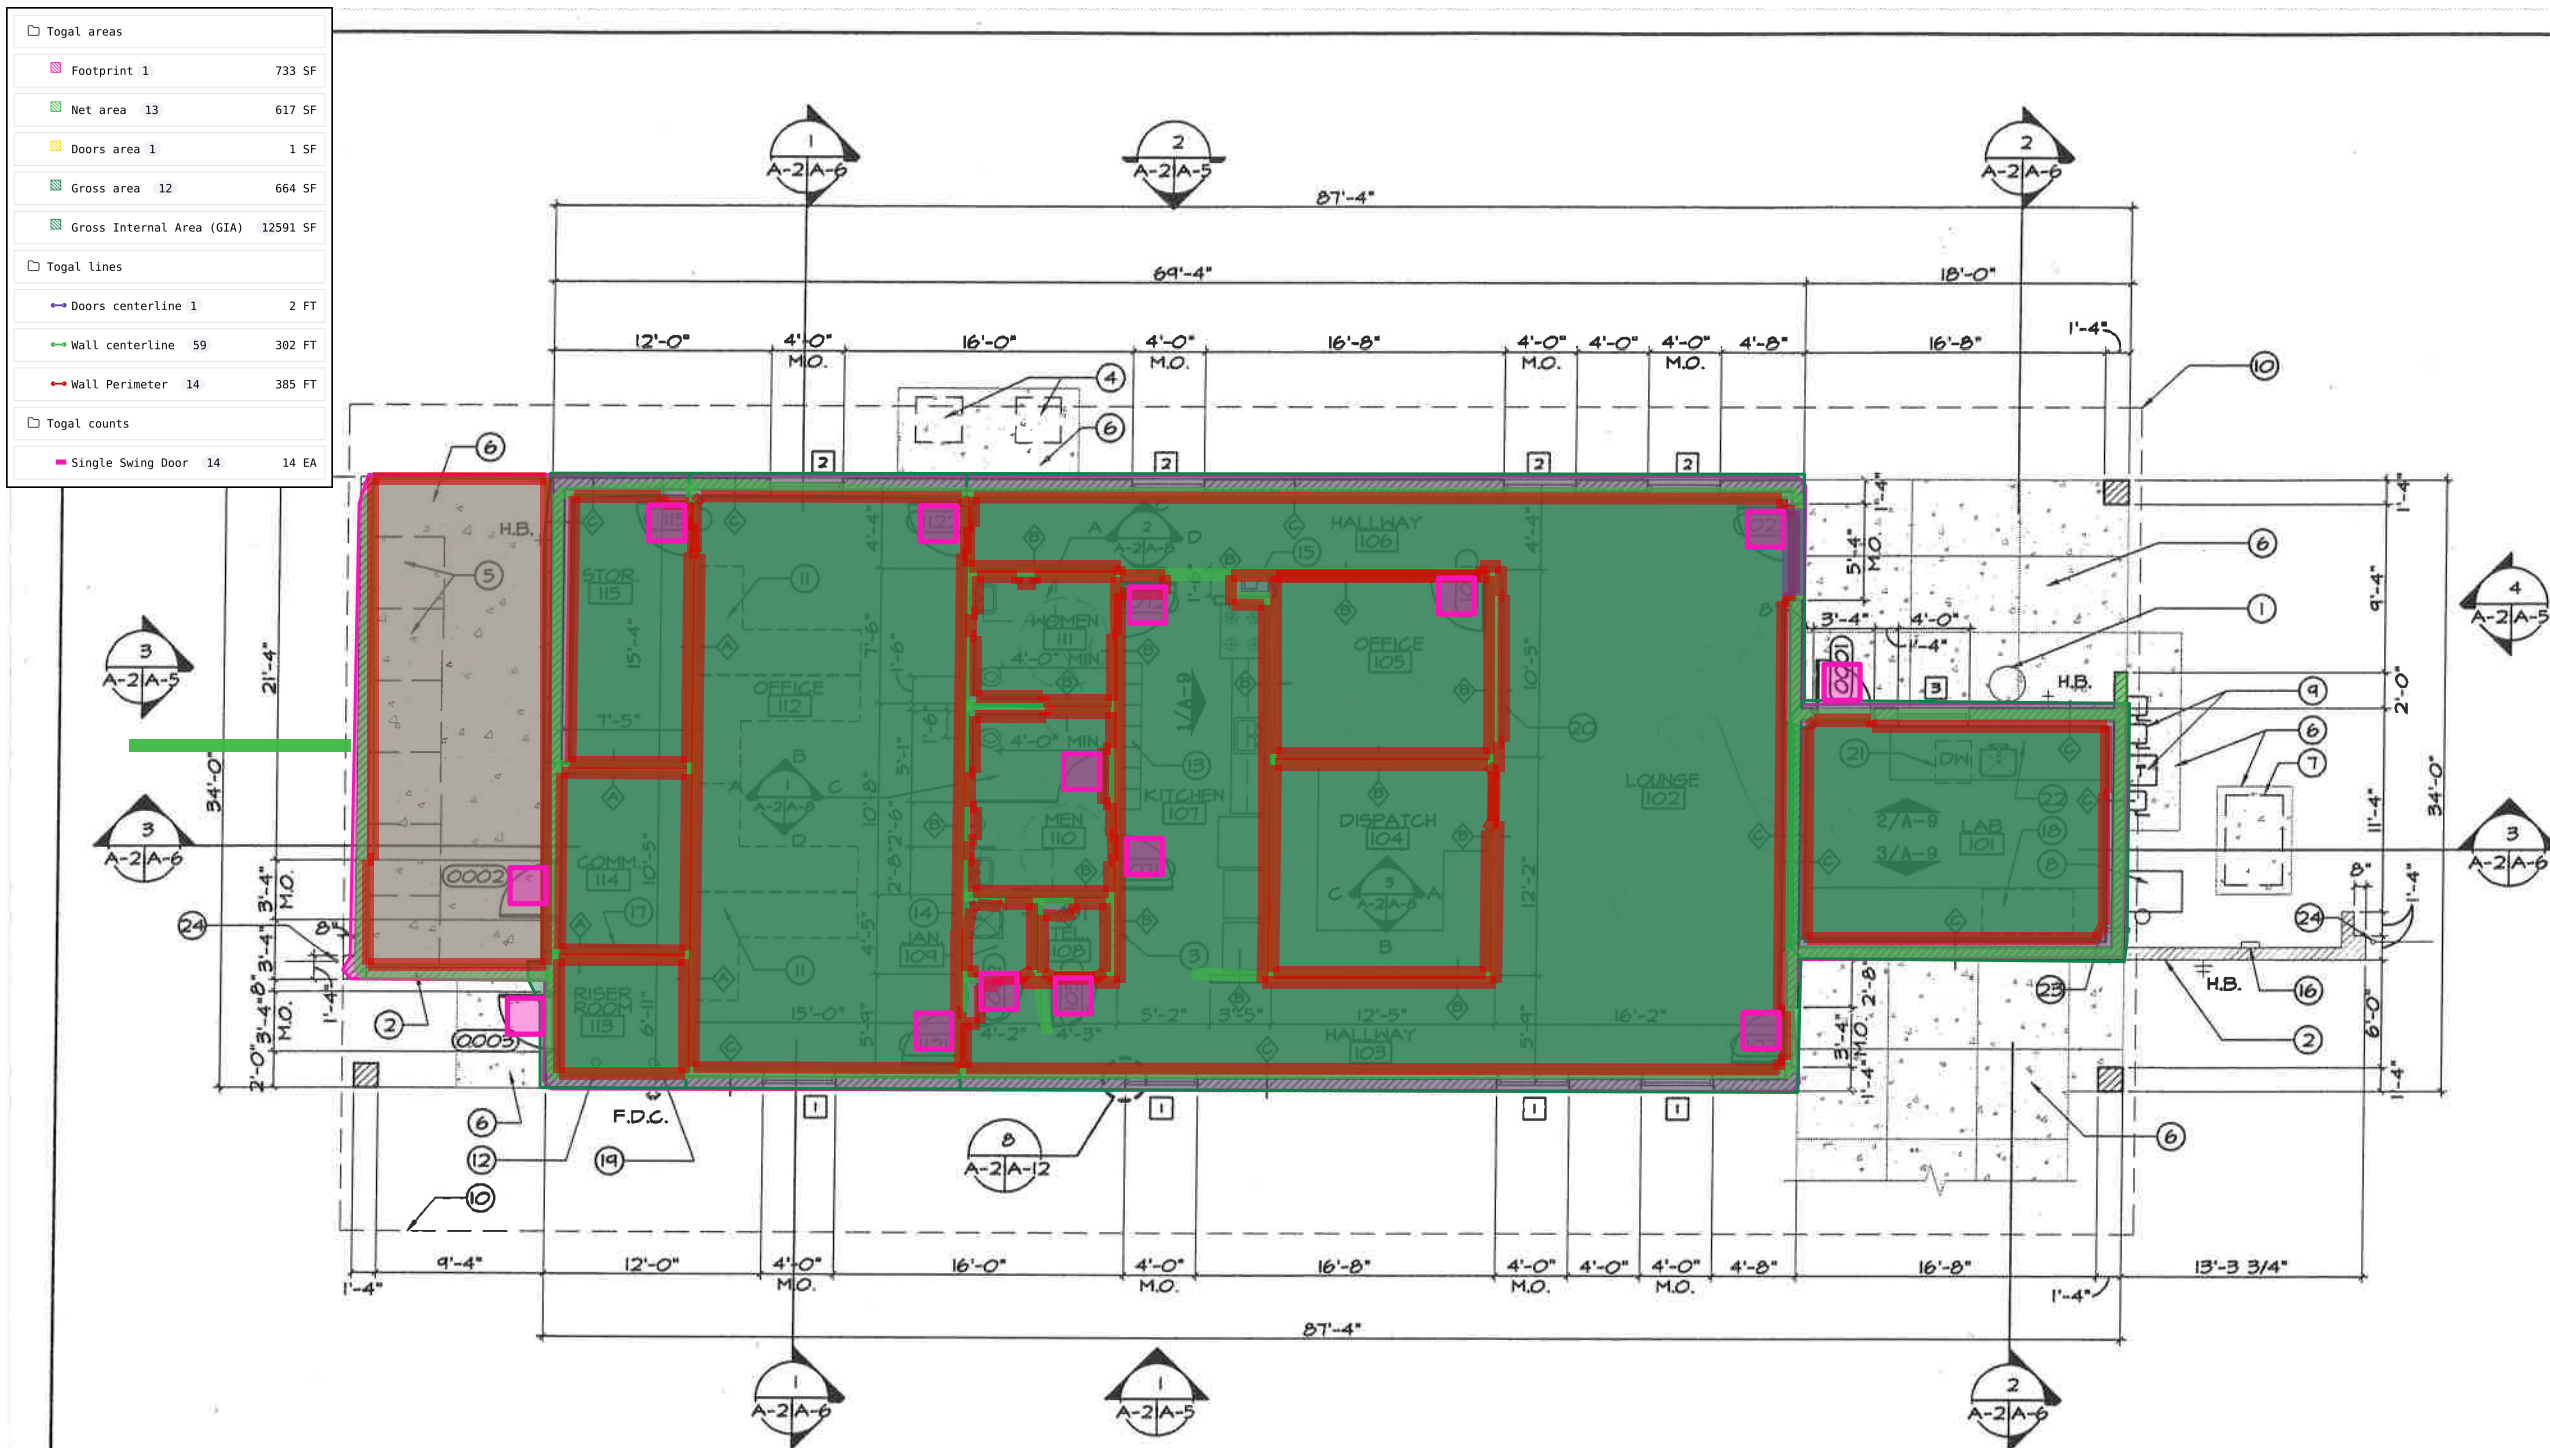

- ## FLOOR PLAN KEY NOTES
- (1) OUTDOOR SHOWER AND EYEWASH
 - (2) CMU SCREEN WALL- SEE ELEVATIONS FOR HEIGHT
 - (3) ELECTRICAL PANELS FLUSH MOUNTED IN 6" STUD WALL
 - (4) GROUND MOUNTED HEAT PUMP UNITS REFER TO MECHANICAL DRAWINGS
 - (5) OUTDOOR PALLET RACK STORAGE
 - (6) CONCRETE PAD / WALK
 - (7) GROUND MOUNTED CONDENSING UNIT- REFER TO MECHANICAL DRAWINGS
 - (8) WALL MOUNTED EXHAUST FAN- REFER TO MECHANICAL DRAWINGS
 - (9) ELECTRICAL SERVICE- REFER TO ELECTRICAL DRAWINGS
 - (10) LINE OF ROOF OVERHANGS
 - (11) SYSTEMS FURNITURE (N.I.C.)
 - (12) DOMESTIC WATER RISER- REFER TO PLUMBING DRAWINGS
 - (13) LOCKERS- REFER TO SPECIFICATIONS
 - (14) FLOOR MOP SINK WITH 20 GAL. WATER HEATER MOUNTED ABOVE- REFER TO PLUMBING DRAWINGS
 - (15) ELECTRIC DRINKING FOUNTAIN
 - (16) IRRIGATION CONTROLLER
 - (17) TELEPHONE MOUNTING BOARD
 - (18) 5' LONG EXHAUST HOOD
 - (19) FIRE SPRINKLER RISER
 - (20) BULLETIN BOARD (SUPPLIED BY OWNER, INSTALLED BY CONTRACTOR)
 - (21) DISHWASHER (SUPPLIED BY OWNER, INSTALLED BY CONTRACTOR)
 - (22) COUNTER MOUNTED EYEWASH
 - (23) 1" SLEEVE THRU WALL FOR FUEL DRAIN @ 30" A.F.F.
 - (24) SECURITY FENCE- 2"Ø SCHEDULE 40 PIPE IN CONCRETE FOOTING, REFER TO DETAIL 9/A-10. CENTER PIPE 1'-0" BACK FROM FACE OF MASONRY WALL

 **1 FLOOR PLAN**
SCALE: 3/16" = 1'-0"

WALL LEGEND		
TYPE	DETAIL	DESCRIPTION
		EXTERIOR 8" CMU WALL
	 2/A-II	INTERIOR PARTITION- 5/8" TYPE 'X' GYP. BD. BOTH SIDES 3-5/8" METAL STUD FRAMING, EXTEND TO ROOF STRUCTURE. PROVIDE R-II BATT INSULATION.
	 3/A-II	INTERIOR PARTITION- 5/8" TYPE 'X' GYP. BD. BOTH SIDES 3-5/8" METAL STUD FRAMING, EXTEND WALL TO 9'-6" A.F.F.. PROVIDE R-II BATT INSULATION.
	 4/A-II	INTERIOR PARTITION- FURR OUT CMU WALL W/ 5/8" TYPE 'X' GYP. BD. OVER 3-5/8" METAL STUD FRAMING. PROVIDE SPRAY-ON INSULATION, FRAMING AND INSULATION TO EXTEND TO BOTTOM OF ROOF TRUSSES. PROVIDE TYPE W.R. GYP. BD. AT RESTROOM SIDE OF INTERIOR PARTITIONS

100% SUBMITTAL

DEPARTMENT OF THE NAVY NAVAL FACILITIES ENGINEERING COMMAND SAN DIEGO		SUBMITTED: DESIGN: DRAWN: CHECKED: FP:		SATISFACTORY TO: FAC MNG. OFFICER: DIRECTOR OF ENG.: SW BN FOR COMMANDER NAVFAC		DATE DATE DATE DATE		REVISIONS APPROVED DATE PREP. BY DESCRIPTION STWRL	
SOUTHWEST DIVISION NAVAL FACILITIES YU-0013R2 FUEL FARM BUILDING MARINE CORPS AIR STATION YUMA		FLOOR PLAN							
SIZE D IF SHEET IS LESS THAN 22" X 34" IT IS A REDUCED PRINT- SCALE REDUCED ACCORDINGLY									
P.W.O. NO.		PROJECT LOCATION		CONSTR. CONTRACT NO.		SPEC.		NAVFAC DRAWING NO.	
SHEET 14 OF									
A-2									

